


REVISIONS				
ZONE	REV.	DESCRIPTION	DATE	APPROVED
-	A	MAJ PM R10233 DEVIENT H16067-100-06 (C100062)	03/09/24	

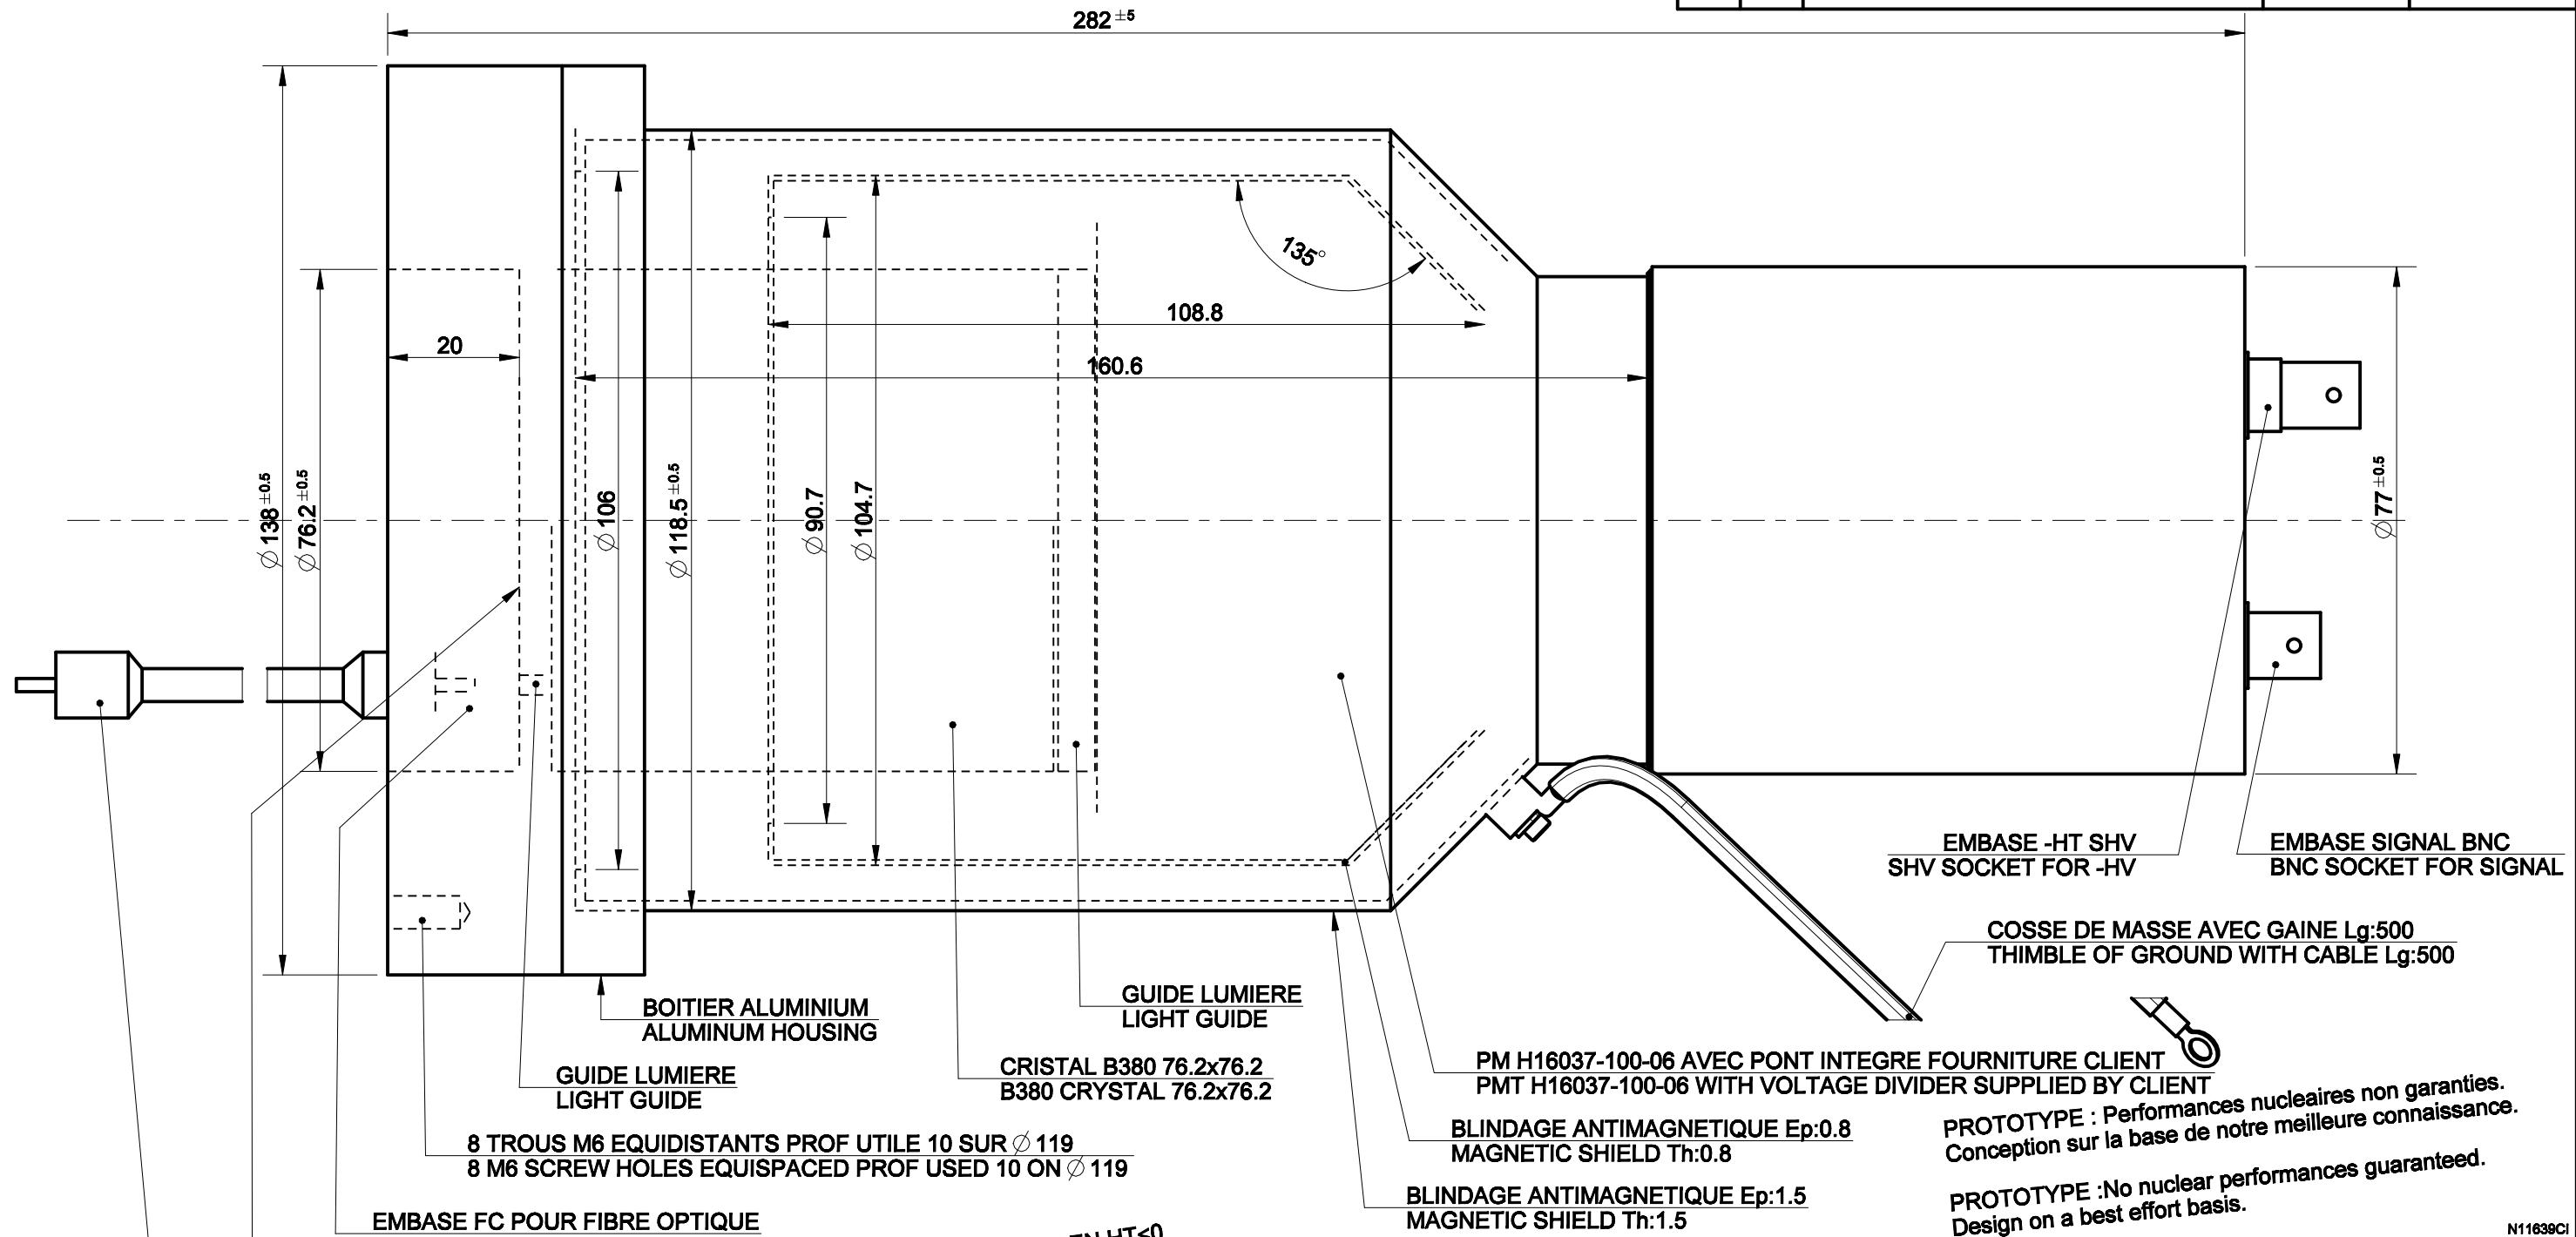

FIBRE OPTIQUE : CENTRE PURE SILICE Ø 1, DEPOT SILICE DOPEE, PROTECTION POLYMER, ENVELOPPE TEFLON TRANSPARENT, PROTECTION PVC NOIRE : Lg:3000
OPTICAL FIBER : PURE SILICA Ø 1 COR, DOPED SILICA CLADDING, POLYMER BUFFER, TRANSPARENT TEFLON JACKET, BLACK PVC PROTECTION : Lg:3000

BLINDAGE ANTIMAGNETIQUE: Matière: Mu-Métal
Composition: 80% Nickel / 15% Fer / 5% Molybdène

MAGNETIQUE SHIELD : Material : Mu-Métal
Composed : 80% Nickel / 15% Iron / 5% Molybdenum

MONTAGE EN HT<0
NEGATIVE USED

☐	APPROVED
☐	APPROVED AS NOTED
☐	REVISED & RESUBMIT
CUST. INIT. _____	
DATE _____	

ENGINEERING SALES DRAWING

DO NOT SCALE THIS DRAWING
THIS DWG IS IN ACCORDANCE
WITH ISO 2768-mK

DRAWN C.J. DATE 13/07/23

THIS DOCUMENT IS APPROVED
AND MAINTAINED UNDER
ELECTRONIC CONFIGURATION
CONTROL



TITLE

76 YLE 76 /3.5 /B380

SIZE	PROJECTION	DWG. NO.	REV.
A3		3-3-8583	A
SCALE 1:1	APPROX. WEIGHT 6.054 kg.	SHEET 1 OF 1	

THIS PRINT IS THE EXCLUSIVE AND CONFIDENTIAL PROPERTY OF LUXIUM SOLUTIONS SAS AND IS NOT TO BE FURTHER REPRODUCED OR DISCLOSED TO ANOTHER PARTY WITHOUT PRIOR WRITTEN PERMISSION FROM LUXIUM SOLUTIONS SAS COPYRIGHT RESERVED. LUXIUM SOLUTIONS SAS 2024

PROTOTYPE : Performances nucléaires non garanties.
Conception sur la base de notre meilleure connaissance.
PROTOTYPE : No nuclear performances guaranteed.
Design on a best effort basis.

N11639CI
3-3-7180